

Bike Stands for Cycle Storage

Toastrack in stainless steel



Notes for Bike Stand:

- Bike storage layout as per Londons Plan SPD and Sutton's council requirements.
- Sheffield stands used.
- 1000mm centre line gaps between stands.
- Stands are 750mm tall x 750mm wide. Made from 50mm o/d tube with 2.5mm wall thickness.
- Overground fixing (bolt-down).
- 16 cycle parking's to be provided.

Bike Shelter for Cycle Storage

BDS Cycle Shelter - 16 Space Cycle Shelter




Notes for Bike Shelter:

- Extremely durable and resilient shelter, it has been structurally tested against the harshest conditions found in the UK and approved against BS EN standards
- No-crawl under perimeter with adjustable feet and allows for fixing onto uneven surfaces.
- 50mm box tube to BS EN standards.
- Frame Hot dipped galvanised or polyester powder coated to BS EN ISO 1461:1999 standard finish - any RAL code colour. Or both which is recommended.
- Polycarbonate cover panel including end panels
- Overground fixing (bolt-down).
- 16 cycle parking's to be provided.

Materials for Cycle Storage

Notes for Materiality:


- Bike Shelter - Galvanised steel with powder coated finish Ral 7016 . Polycarbonate cover.
- Bike stand - Stainless steel

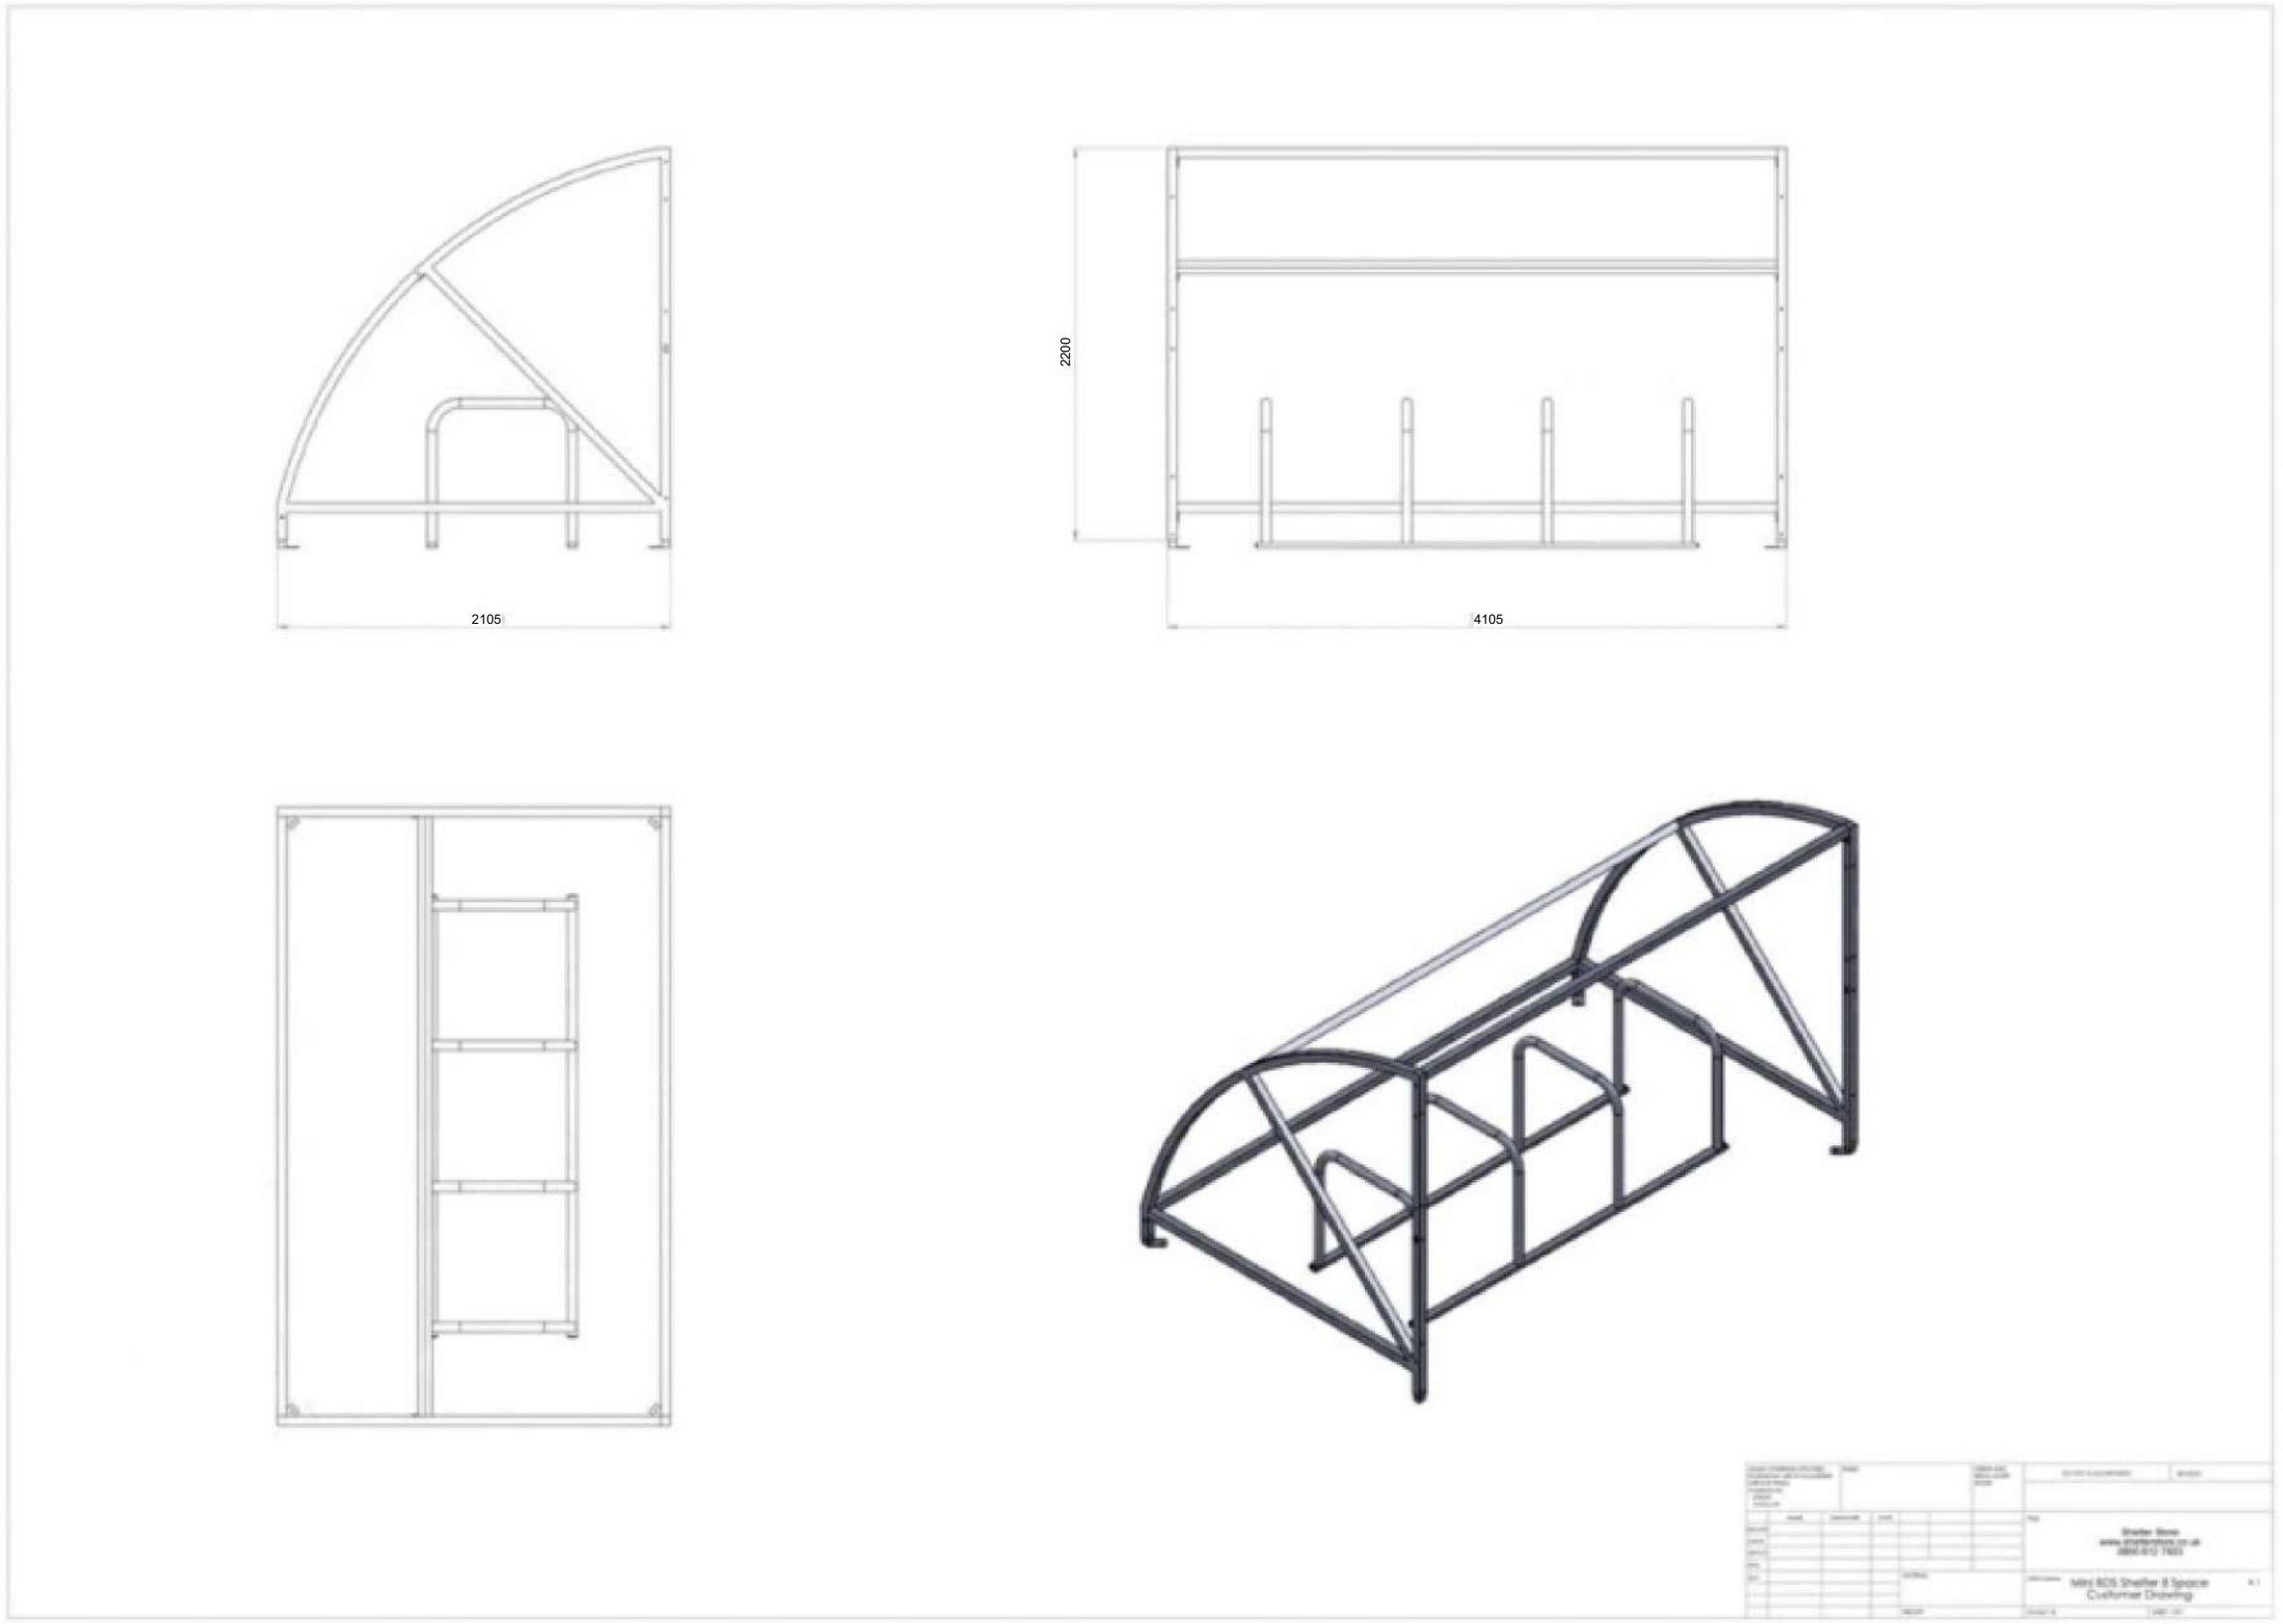

Bike shelter and stand setting out




Example of sheltered cycle storage parking proposed

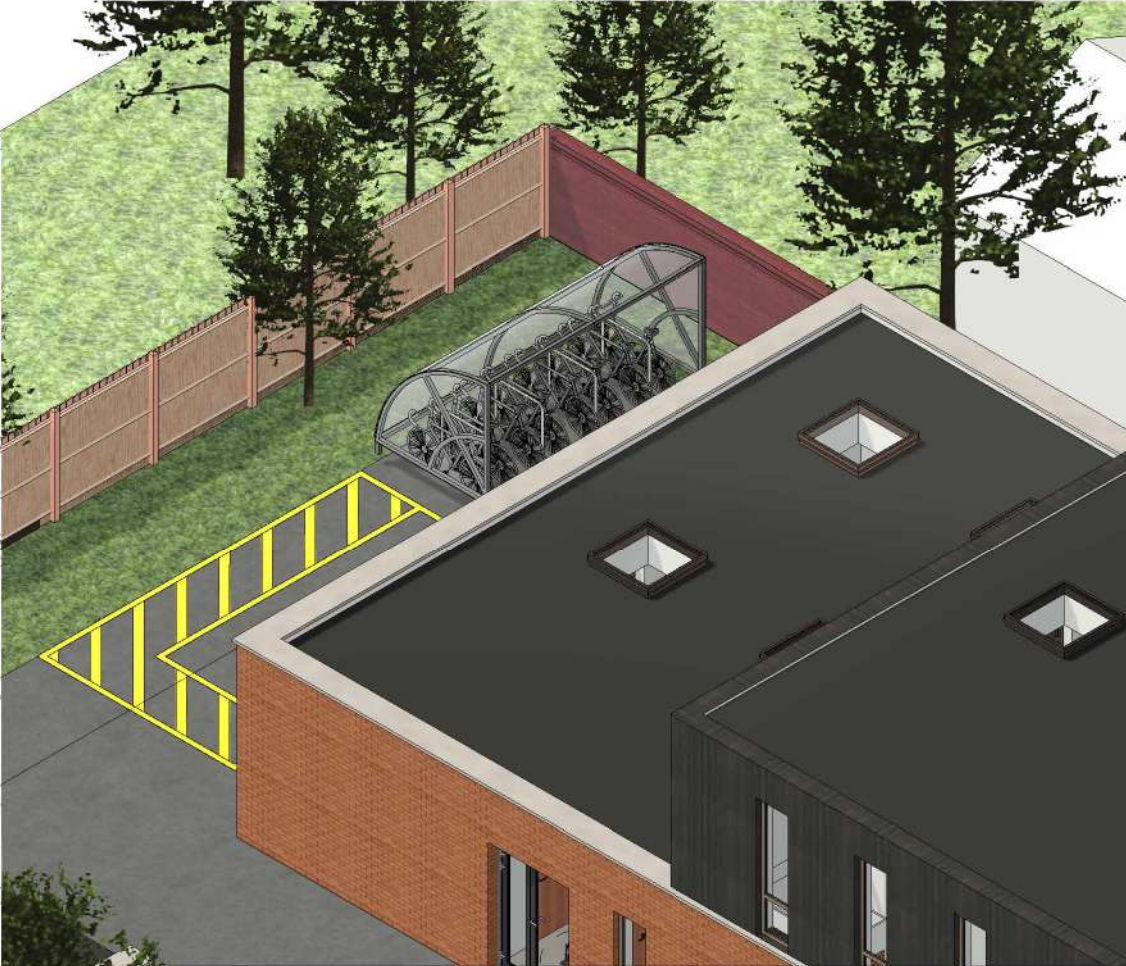


2 CYCLE STORAGE - 3D VIEW 01



4 CYCLE STORAGE - 3D VIEW 02

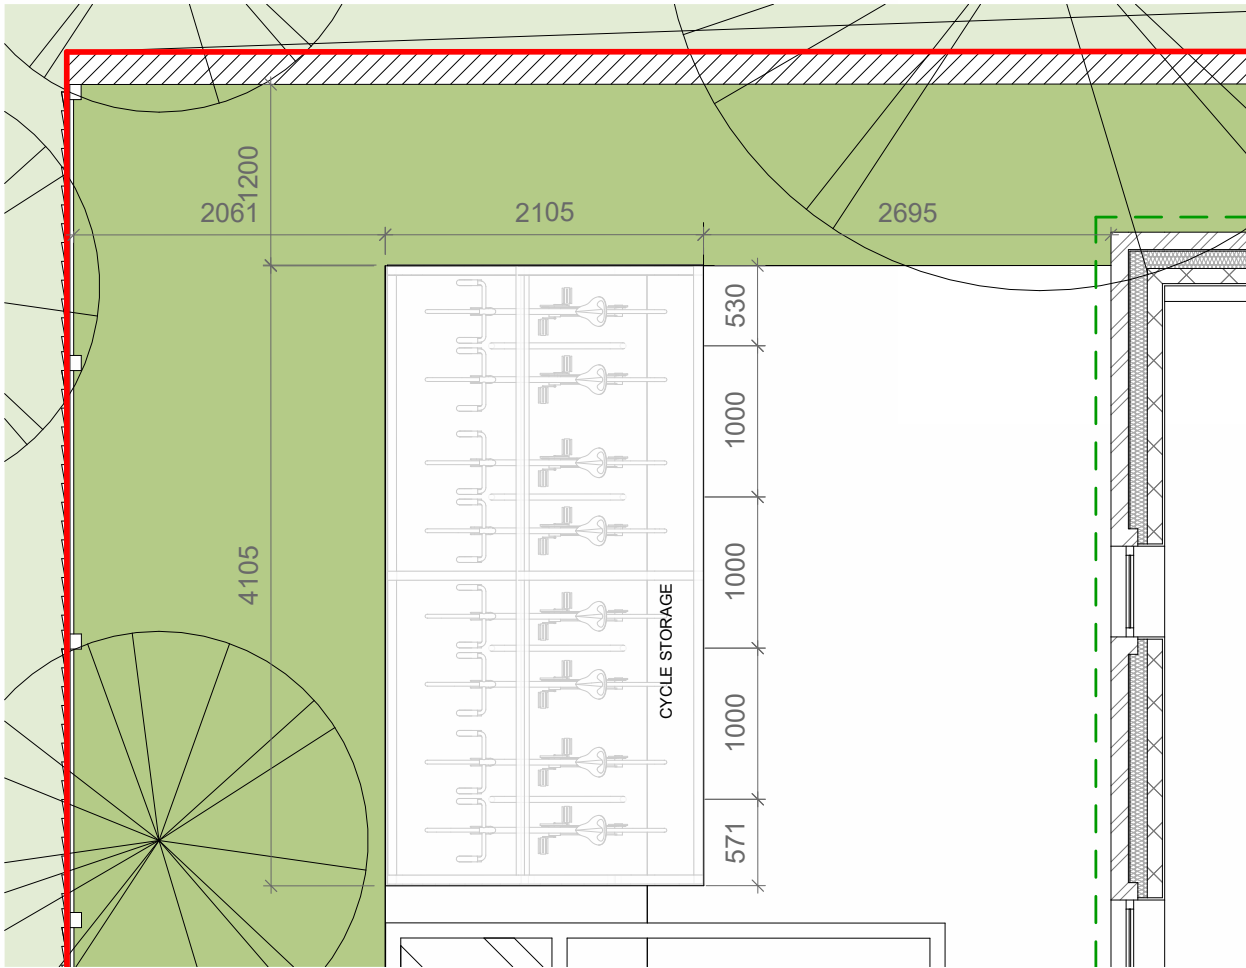

1 Proposed Site Layout Plan
1 : 50

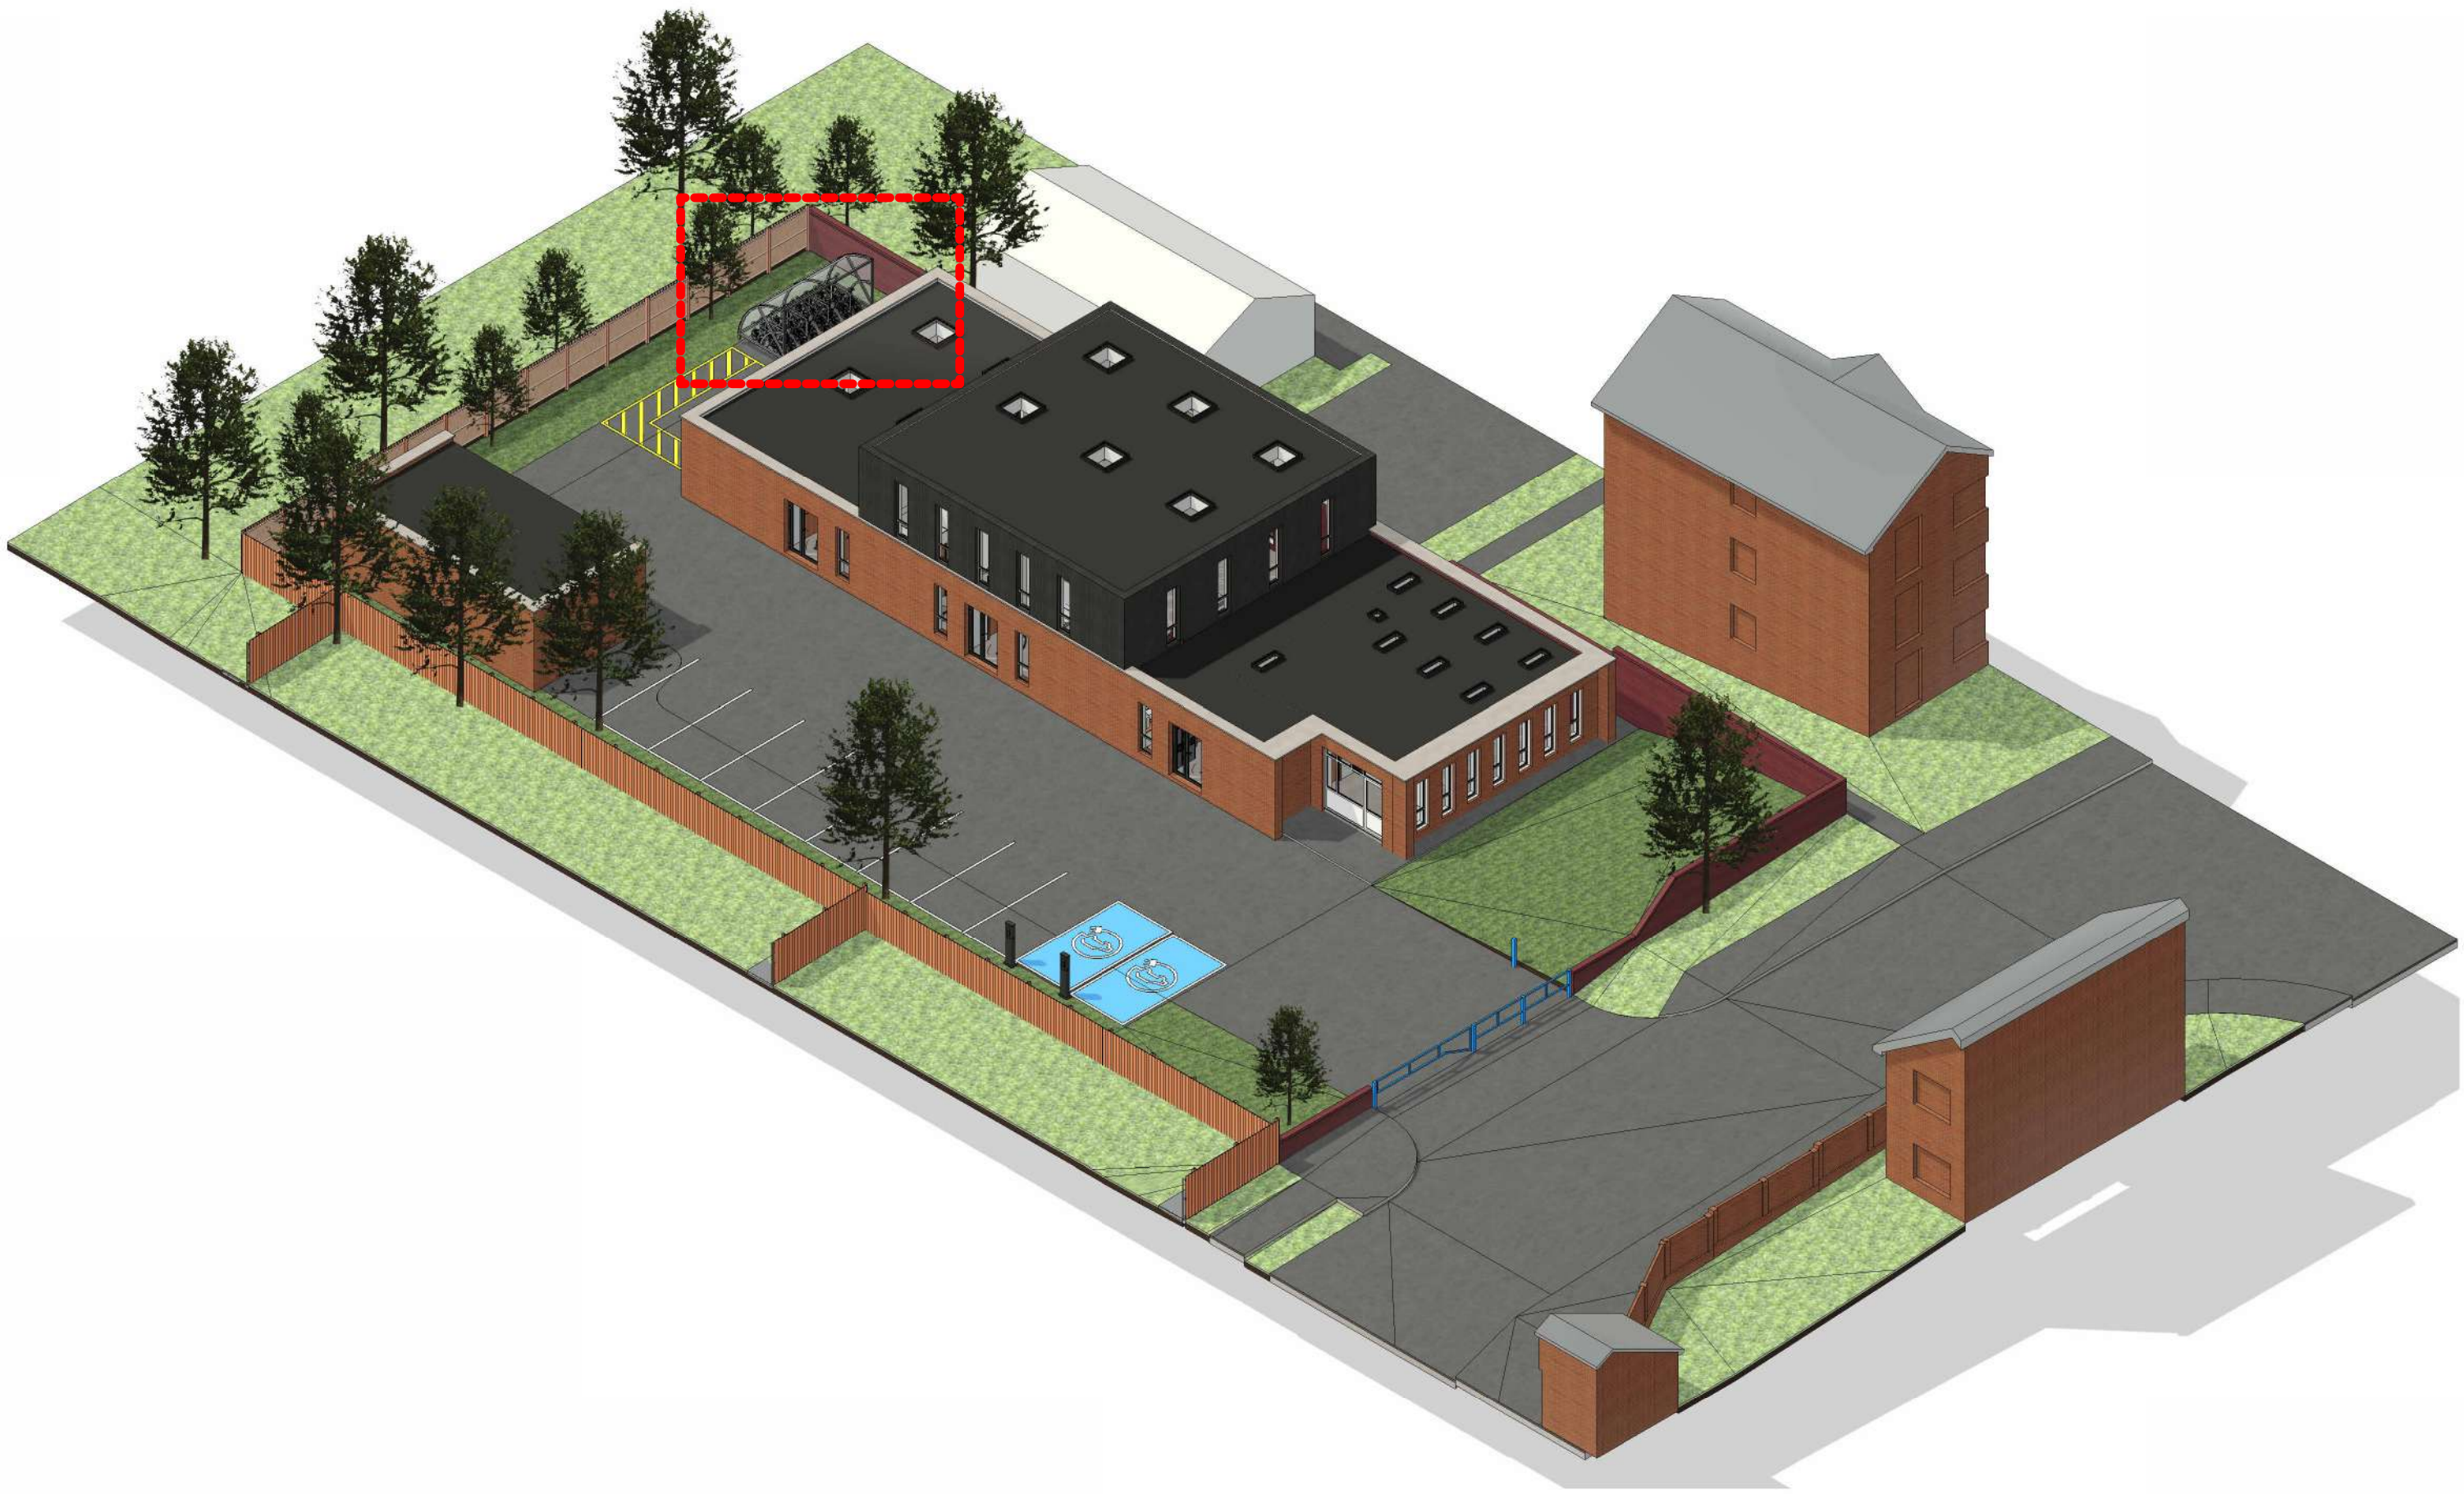

3 CYCLE STORAGE LOCATION

General Notes:

- Cycle storage compliant with Sutton Council cycle storage guidelines.
- Easy wash down design.
- Appropriate foundation and flooring to be used/ installed as per installation guidelines and to SE details.
- Concrete bases and pad footings to structural engineers details.
- Refer to all notes on drawing for detailed information for the whole cycle storage.
- Appropriate signage to front of cycle storage.

No.	Description	Date	Issued by

