




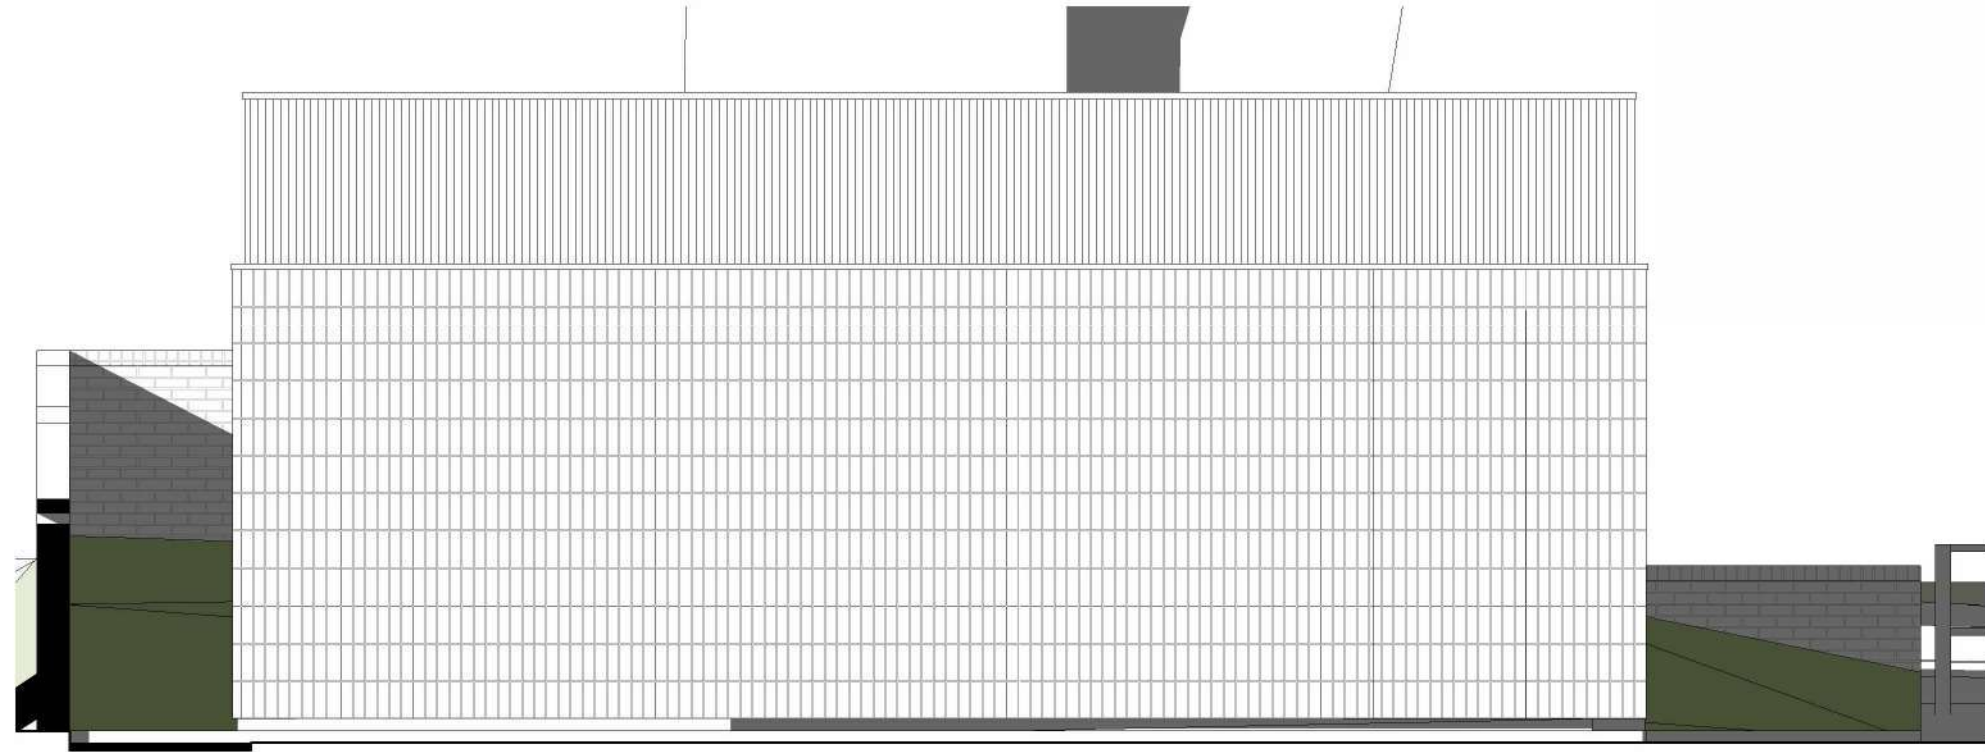


① Existing North (Rear) elevation
1 : 50

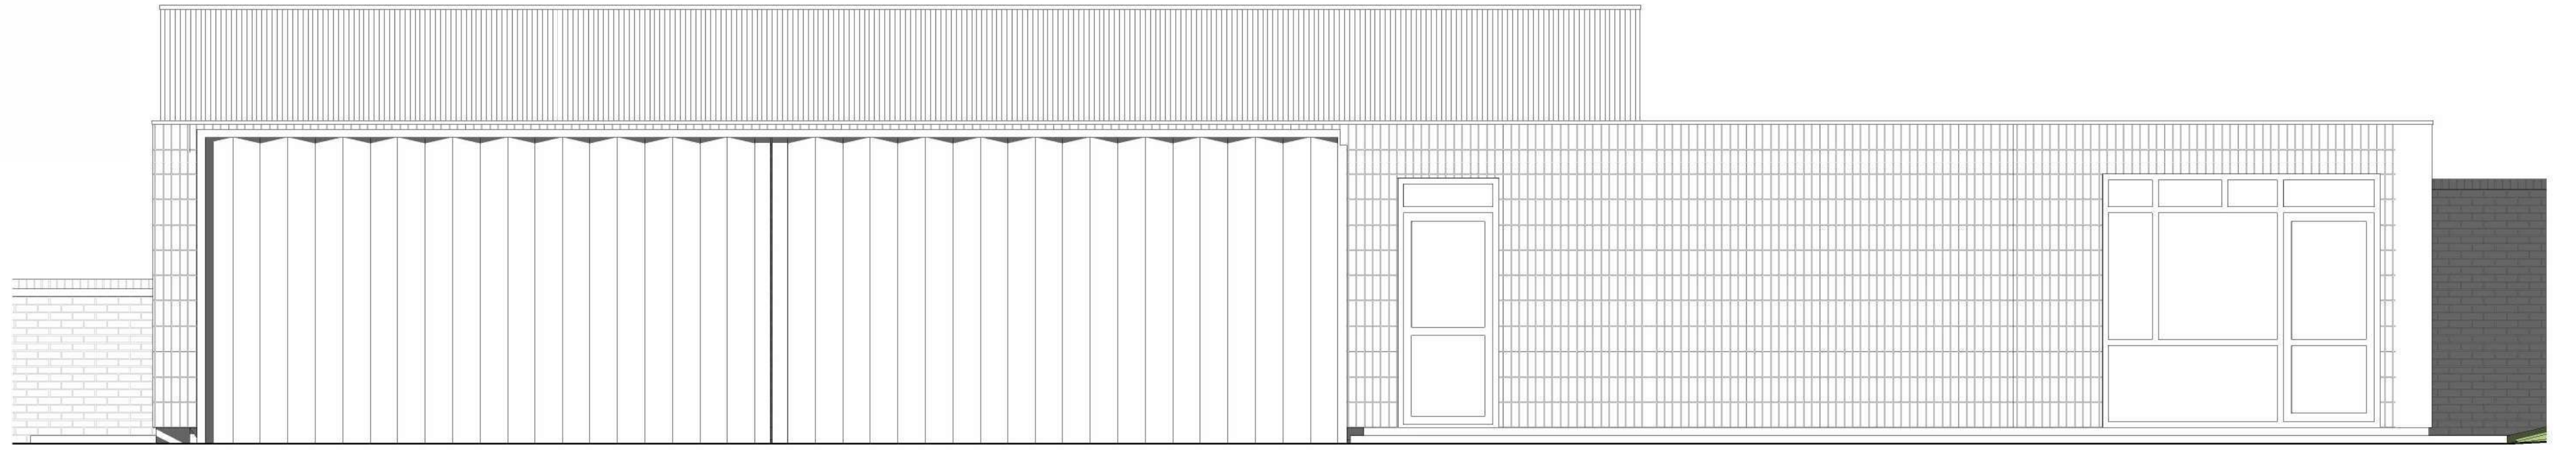


③ Existing West (Left Side) elevation
1 : 50

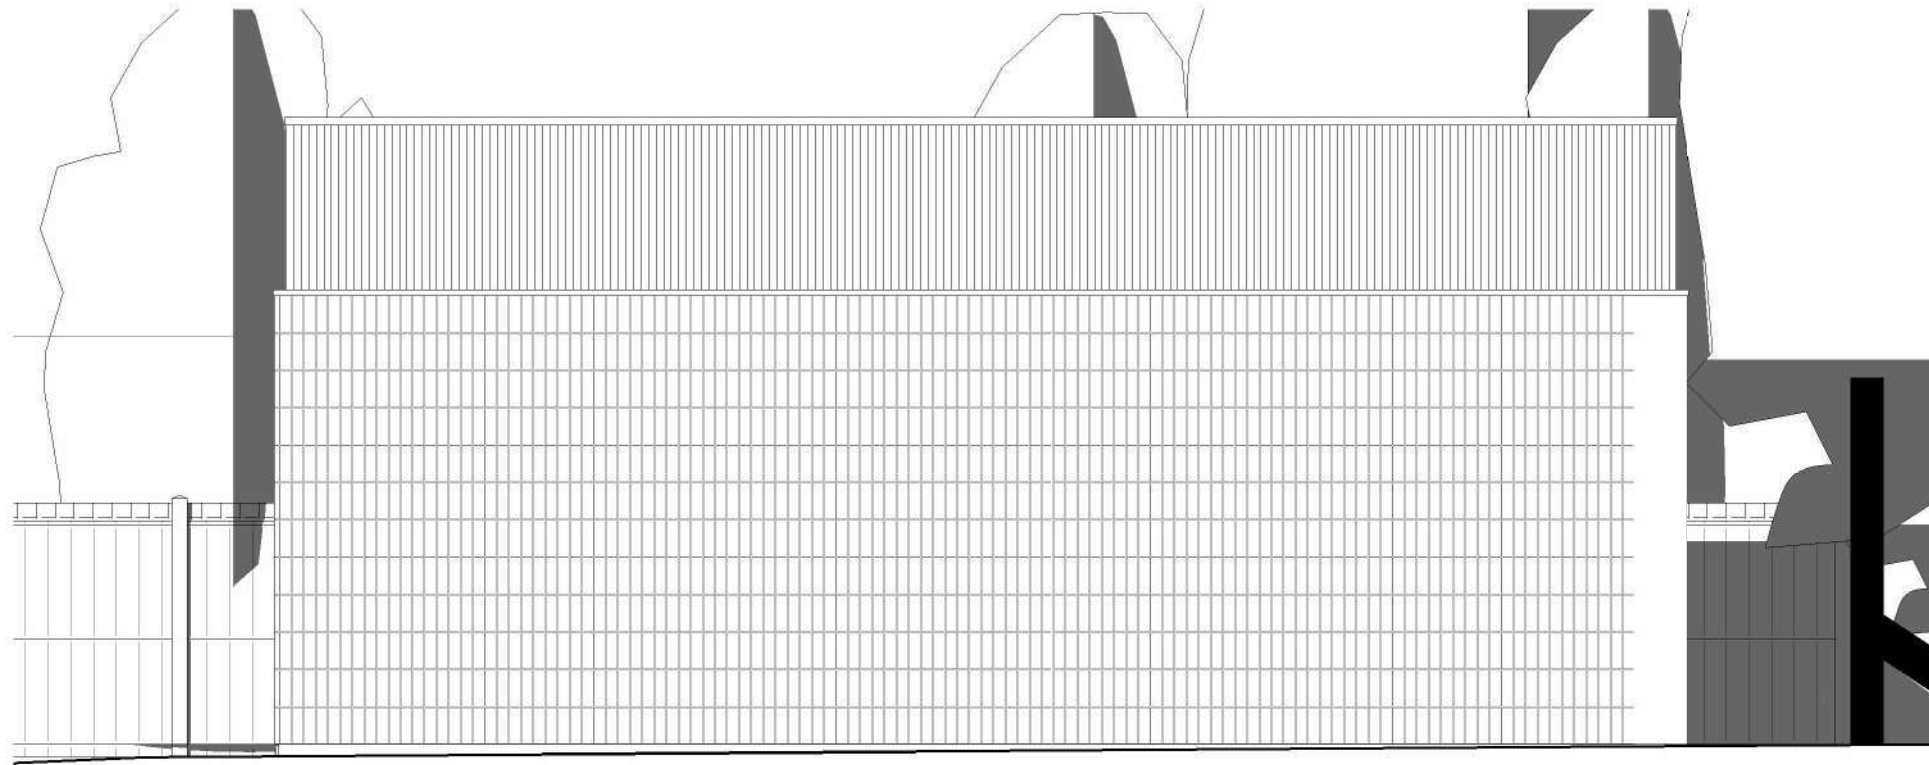


② Existing South (Front) elevation
1 : 50

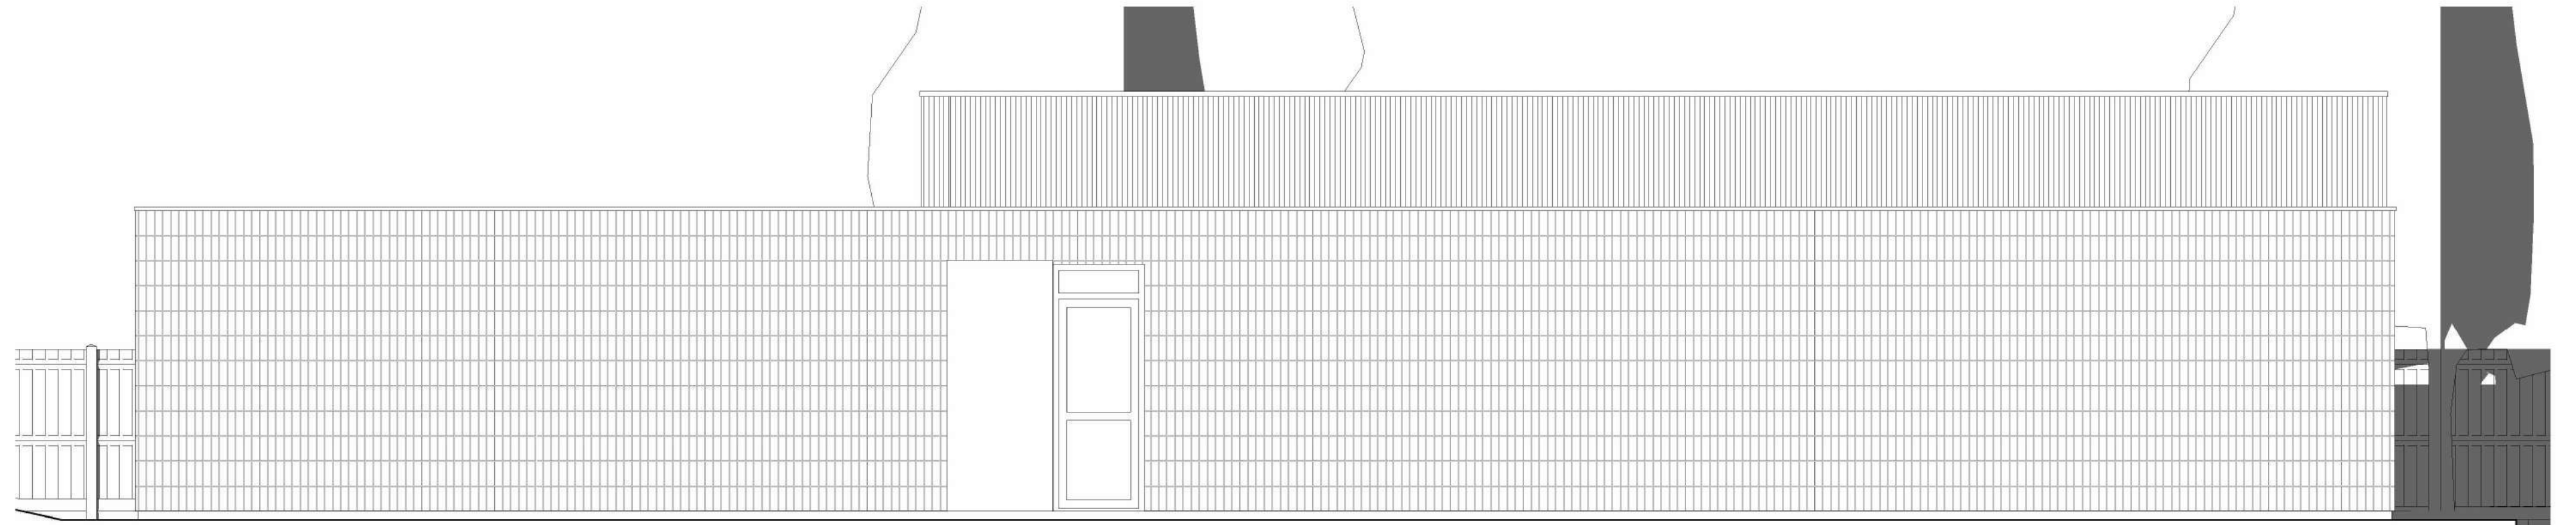


④ Existing East (right side) elevation
1 : 50

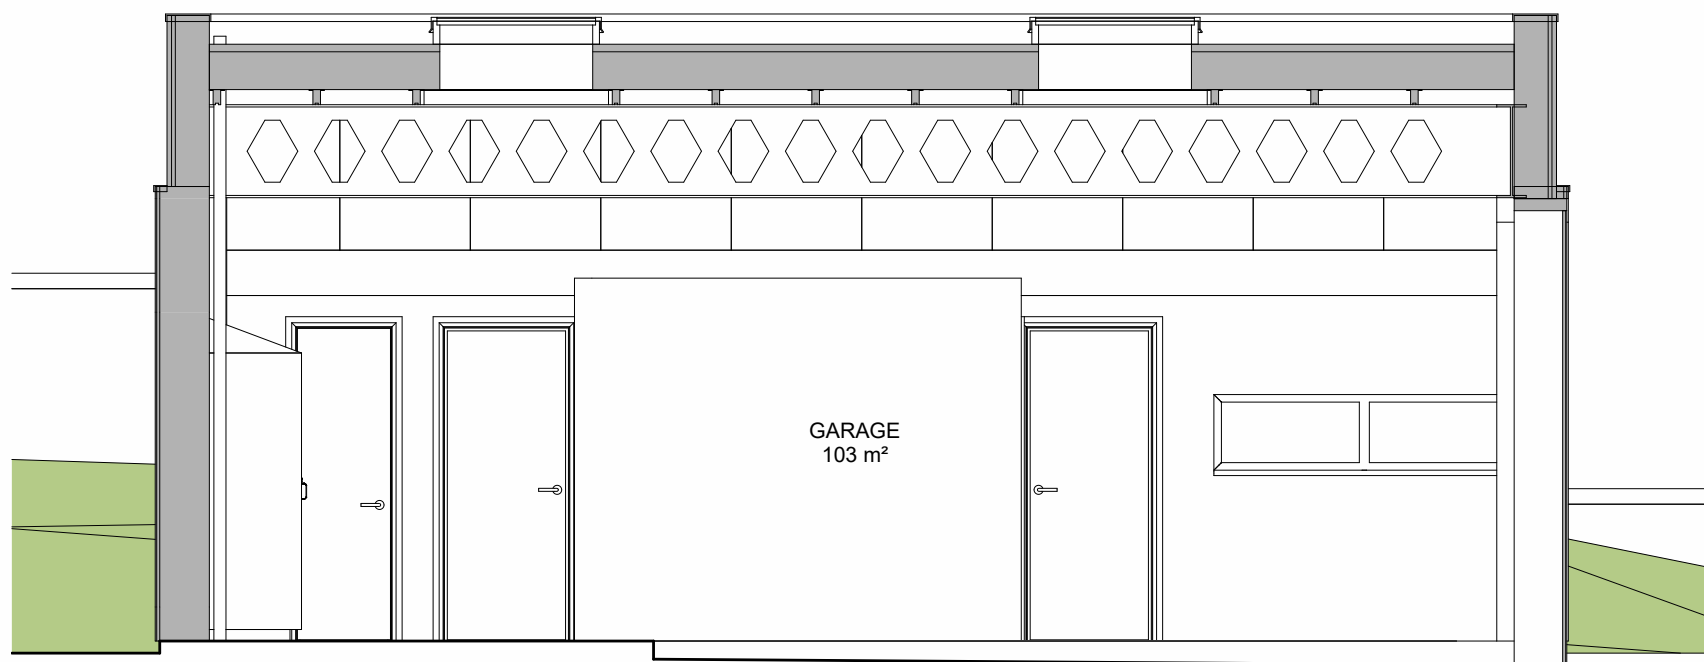



⑤ Section 1
1 : 50

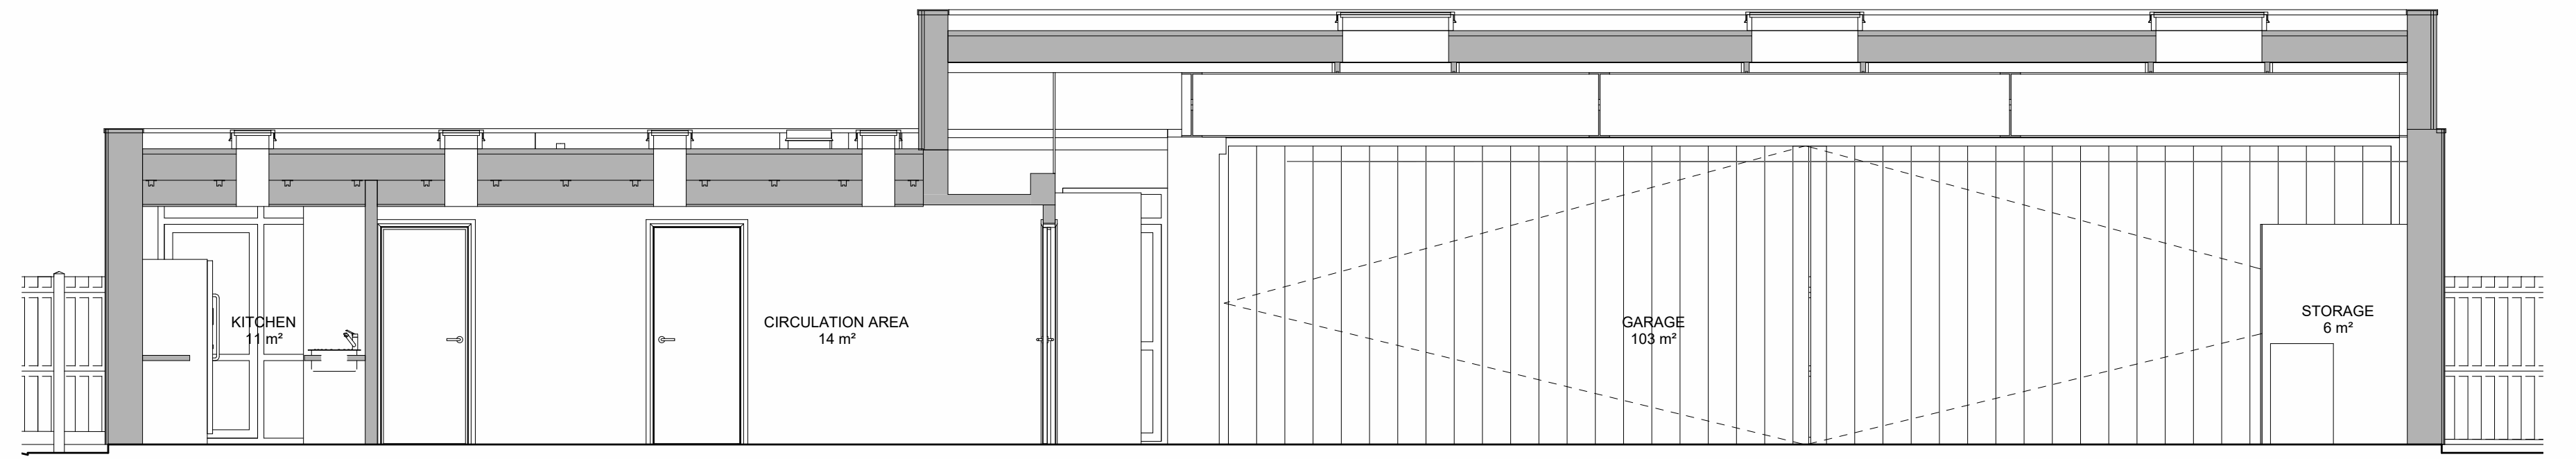

⑥ Section 2
1 : 50

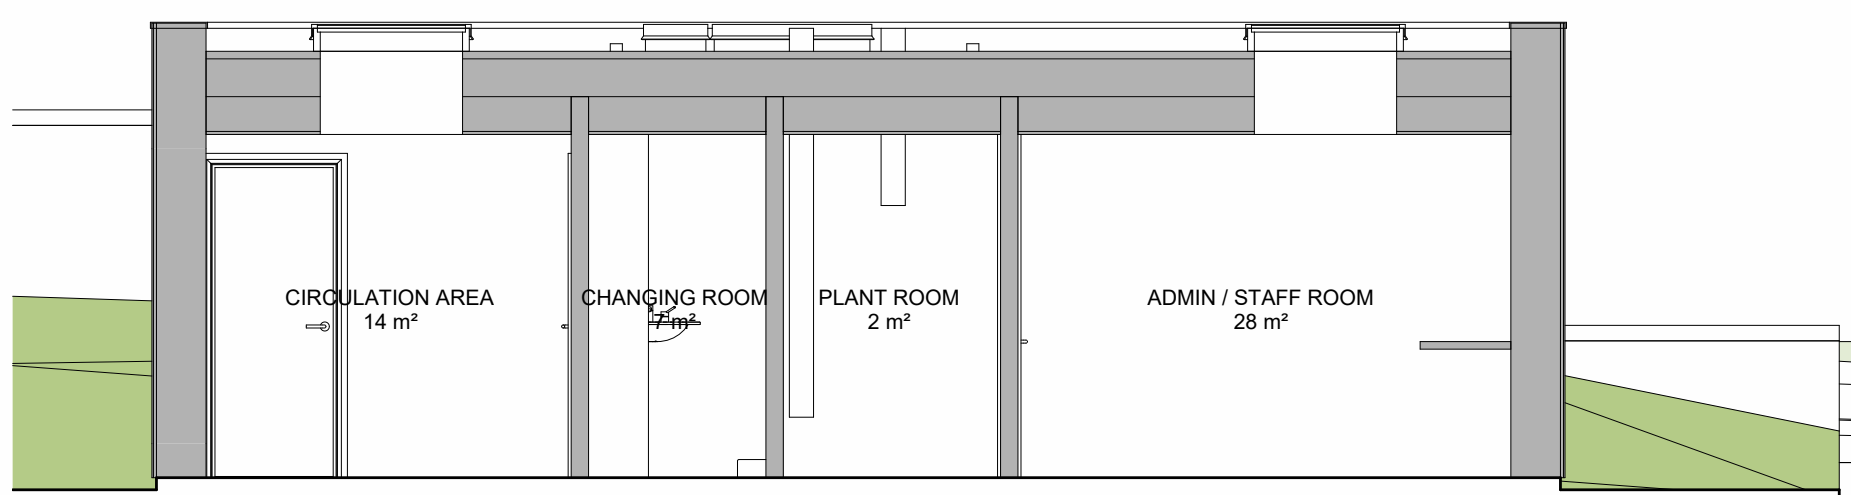

⑦ Section 3
1 : 50

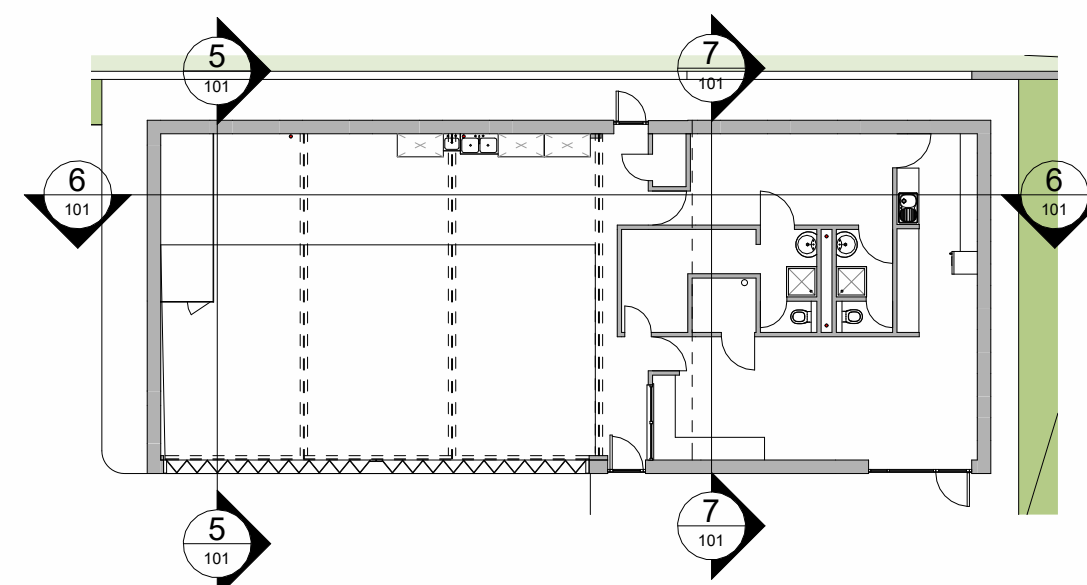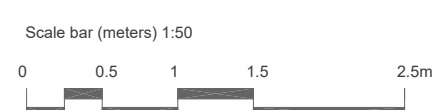

⑧ Key - Existing Ground Floor Plan
1 : 200

Survey Drawing

THE TRUSTEES BASMA

Project: CHANGE OF USE FROM SUI-GENRIS TO USE CLASS F1&F2
Address: SUTTON AMBULANCE STATION, DORSET ROAD, SUTTON, LONDON, SM2 6JH
Drawing title: EXISTING NORTH, WEST, SOUTH & EAST ELEVATIONS AND SECTIONS

Scale: As indicated @ A1
Date: 29/05/25
Drawn by: MA / OI
Drawing num: 786/BASMA/SU -101
Rev:

Office 3 (Ground floor) 679-691 High Road, Leyton, London E10 6RA
Tel. 020 8558 4272