

Locking Mechanism for Refuse Storage



Lockey 2500 S Surface Mortice Hook digital lock for sliding doors (OR SIMILAR APPROVED)
2500 S
Specification
Body material - satin chrome finish
Door material - Suitable for aluminium doors
Weather resistant and external use


Non handed - Lock will fit doors hung on the left or right

Notes for Locking Mechanism:

- Locking mechanism specified or similar approved to be used.
- Locking mechanism to be full weather proof to the elements (IP65).
- Full tamper and vandal proof.
- High durability.
- Easy key-less system for ease of use.
- Lock combination to be given to the personnel who would be using this refuse.
- Lock combination to be given to the council waste services once installed so they can have access to the refuse area for waste collection.
- Any change in combination to be notified to the council waste management team.

Refuse Bins for Refuse Storage

2 x 1100L AND 2 x 240L *Euro bins to be used*

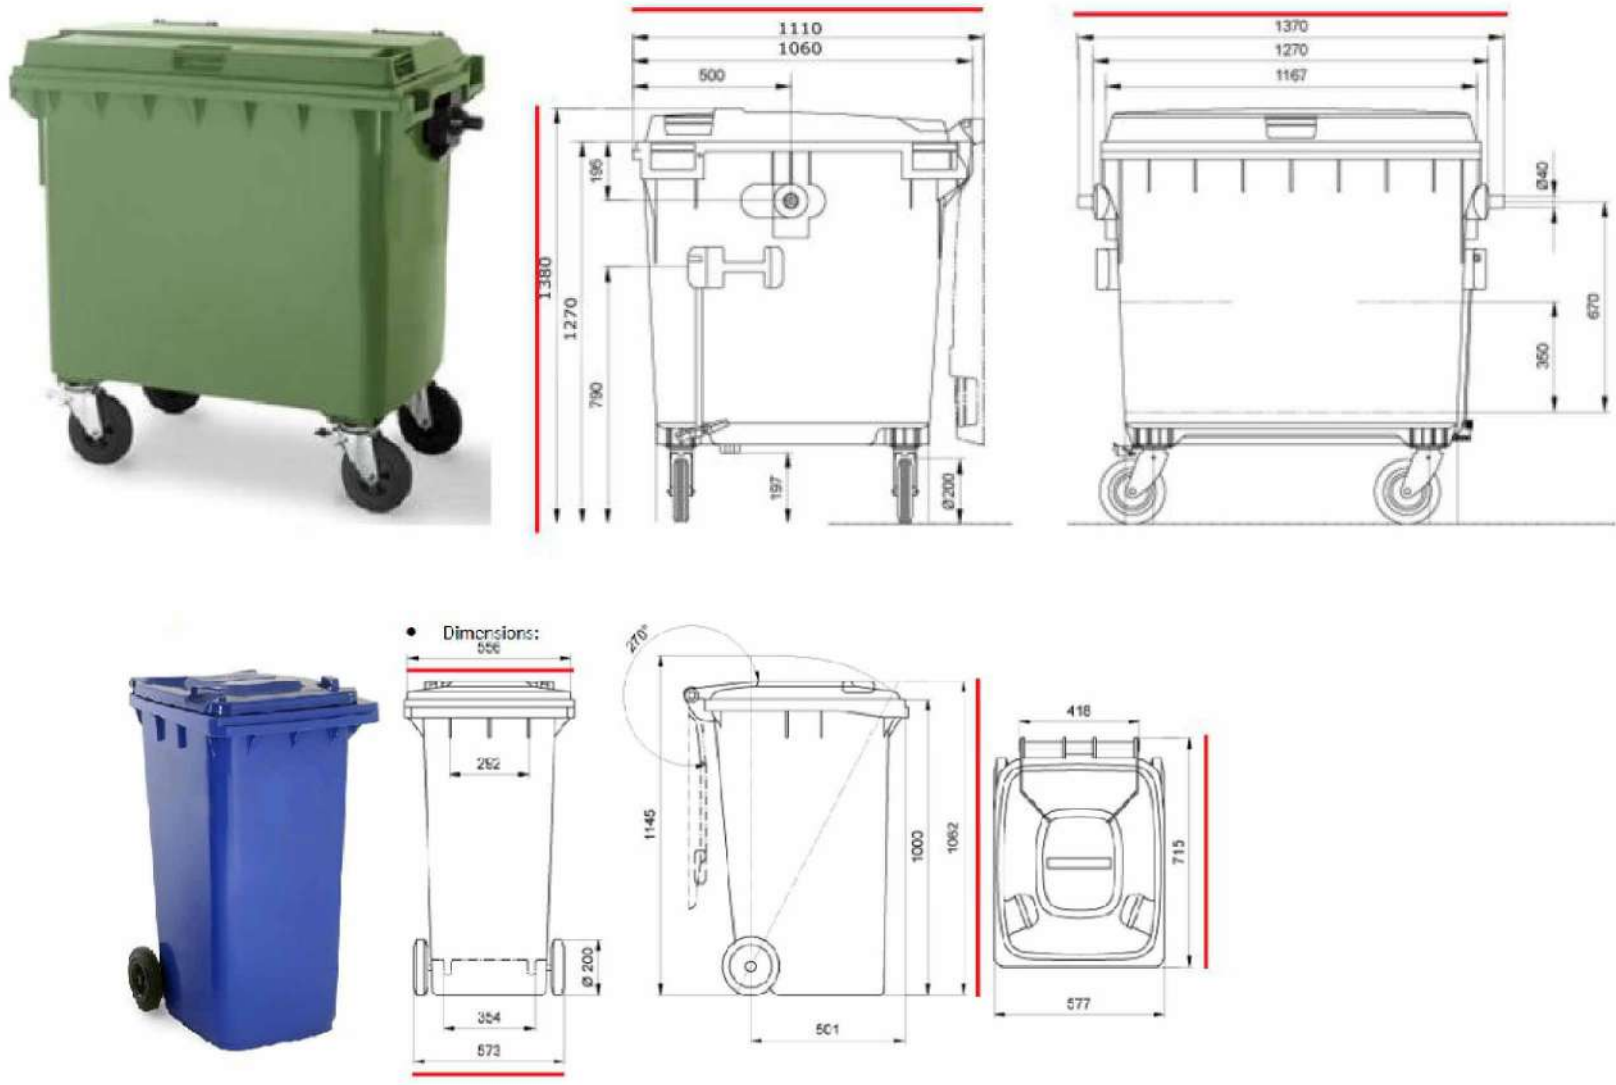

Notes for Refuse Bins:

- Refuse storage capacity compliant with Sutton Council waste management guidelines.
- Refuse storage capacity as per proposed outlined in approved Design and Access statement.
- 2 No. 1100 and 2 x 240L litres bins provided

Materials for Refuse Storage

Notes for Materiality:

Walls - Timber and brick fencing: to be horizontal slats charred larch timber cladding or similar approved on galvanised steel box posts.
Galvanised steel box posts to SE spec. (\$355 90x90x6.3mm glavanised SHS post at maximum 1500mm centers - fixed to foundation with manufactures details) To inside of garden. Connection to foundation to manufacturers details and spec

Security Lighting for Refuse Storage

Notes for Security Lighting:

- Lighting provided to lit the refuse area
- Refuse storage enclosure to bins. Personnel to enter refuse storage to emitting the bin and need to light internally.
- Drawing to be read in conjunction with structural engineers foundation design requirements.


Ventilation for Refuse Storage

Notes for Ventilation:

- Natural ventilation to be sufficient for the refuse storage as located externally to building.
- Louvre timber enclosure to provide natural ventilation.
- Sufficient space left around bins to allow air flow within refuse storage.
- Minimal odour expected from the 4 bins.


General Notes:

- Refuse storage compliant with Sutton Council Waste Management guidelines.
- Drainage incoperated into design to allow for wash down. To link to existing floor gulley.
- Level access threshold required to allow for easy movement of bins.
- Refer to all notes on drawing for detailed information for the whole refuse storage.
- Rain water drainage from roof to fall into gutter and down pipe. Down pipe to be directed towards a drainage point. Refer to NBS spec R10
- Appropriate refuse signage to front of refuse storage to be installed.
- Drawing to be read in conjunction with NBS specifications F10, F30, H60, D20, E10.

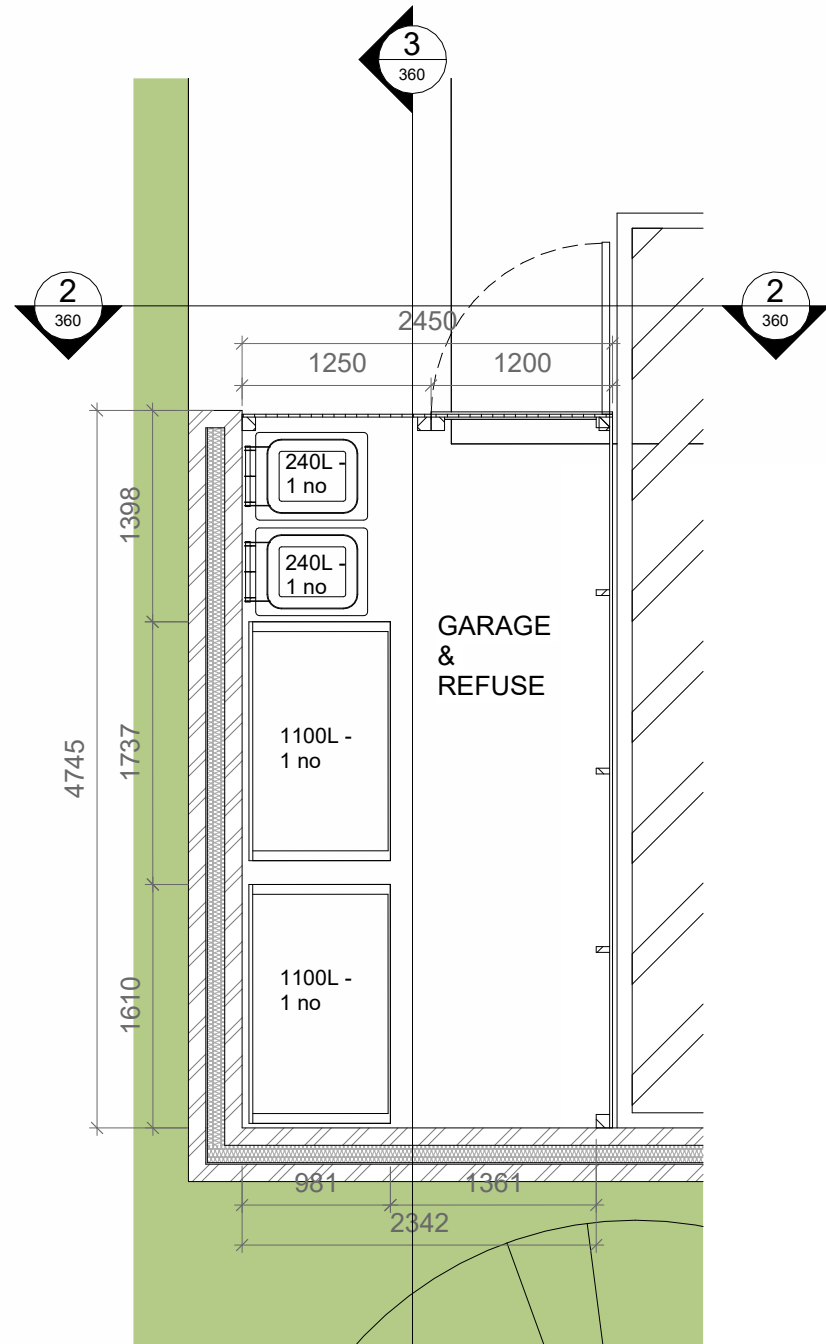

1 Proposed Ground FFL - Refuse
1 : 50

2 Refuse Elevation
1 : 50

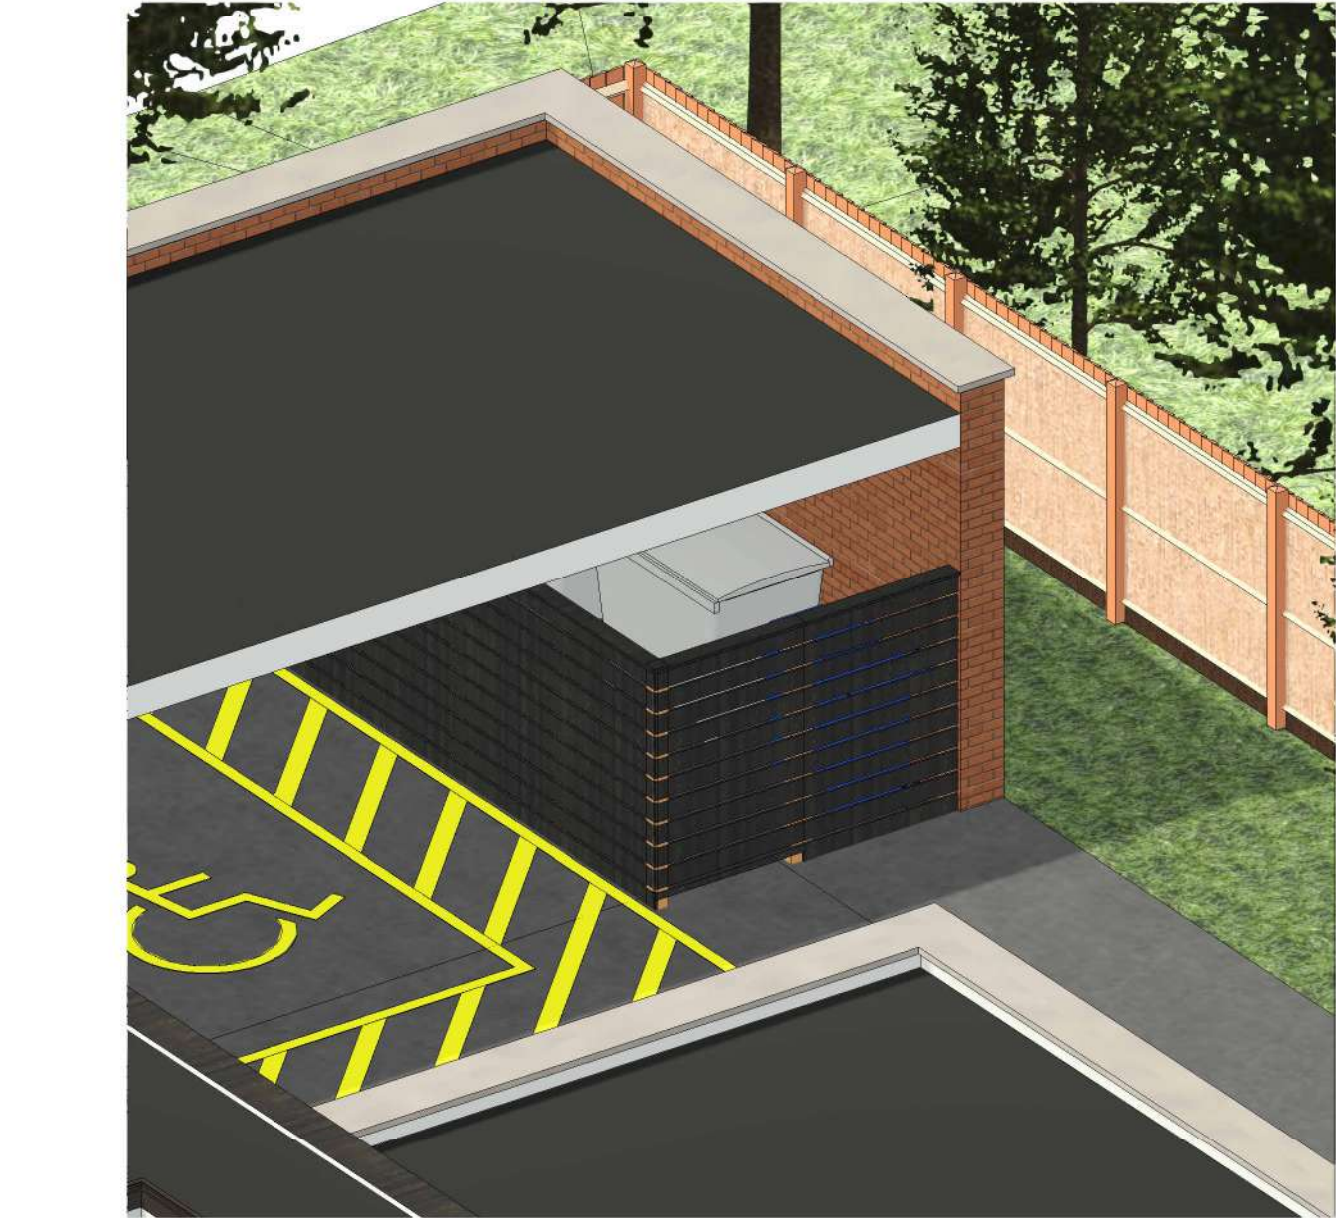


4 Refuse 3D View - 01


3 Refuse Section
1 : 50



5 Refuse 3D View -02

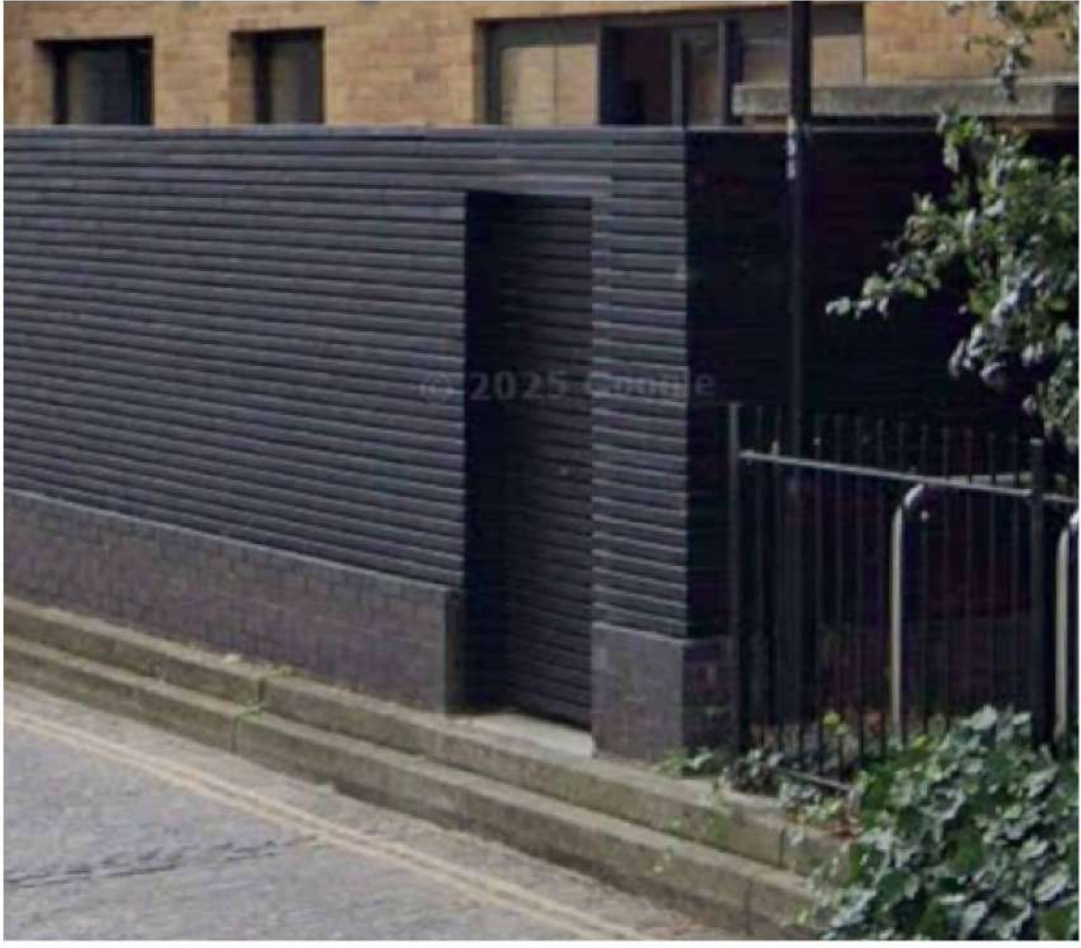

Example of sheltered refuse enclosure proposed

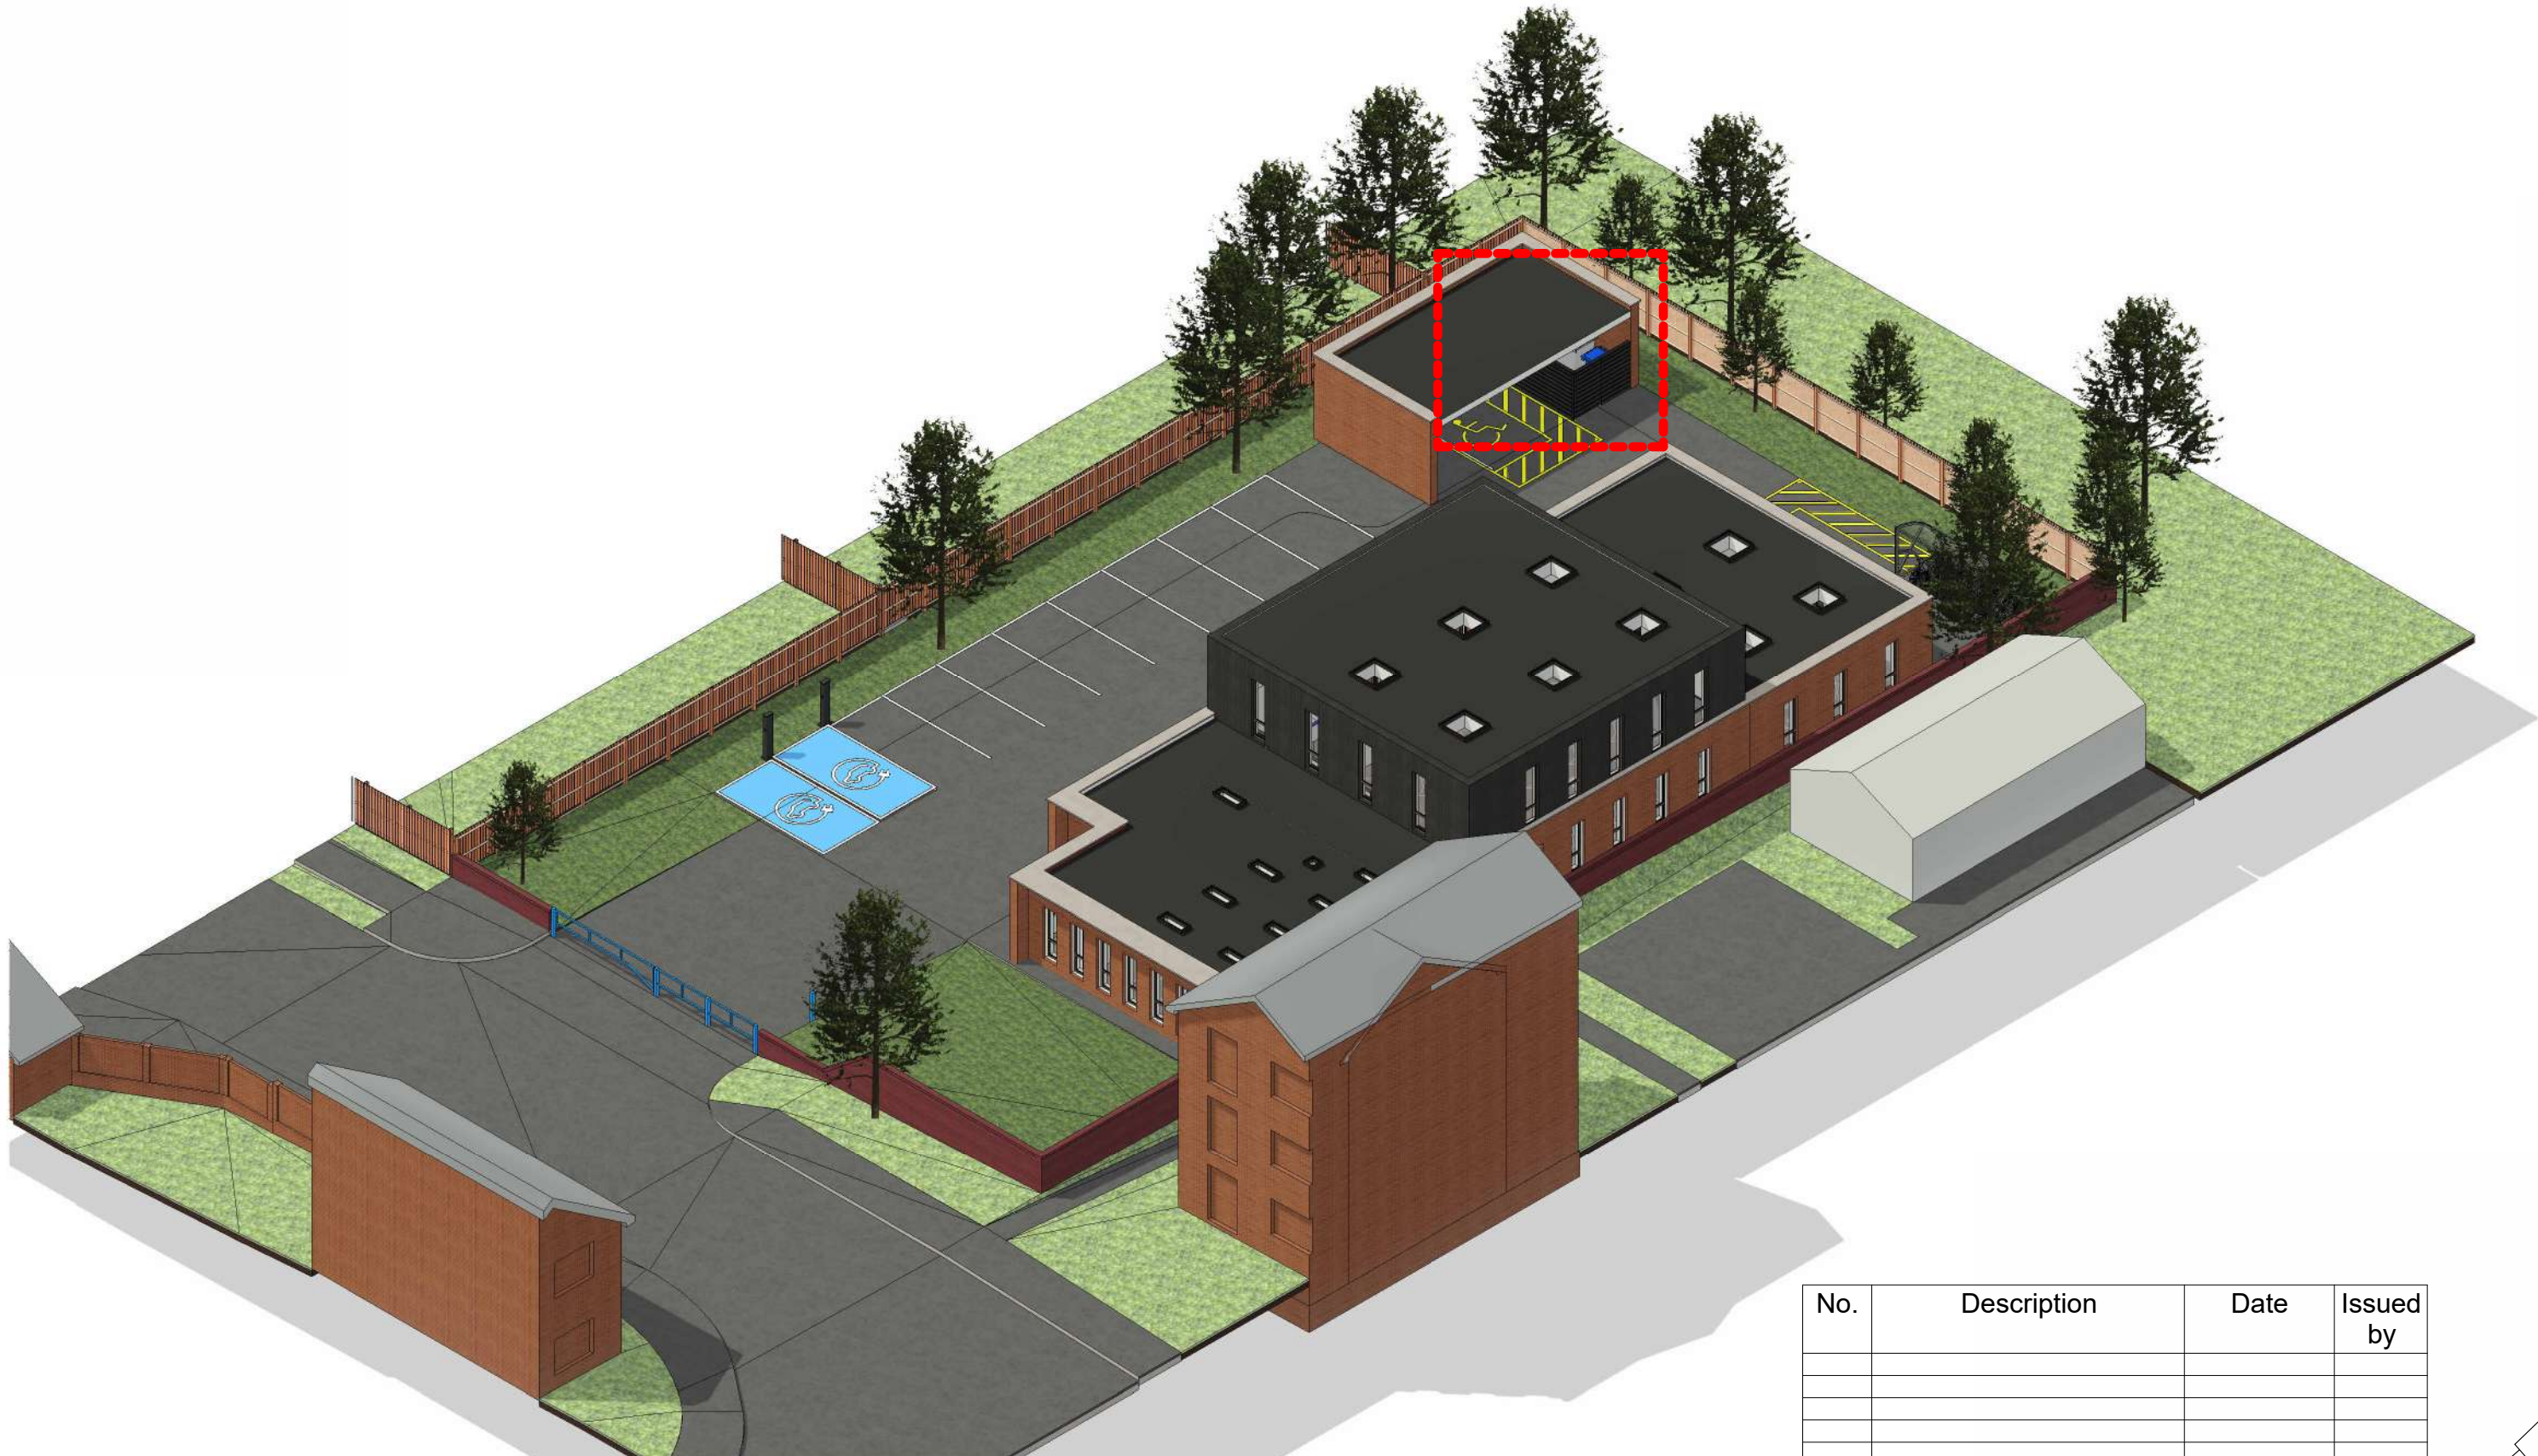

6 Proposed Refuse Location

No.	Description	Date	Issued by

Planning Submission

THE TRUSTEES BASMA

Project: CHANGE OF USE FROM SUI-GENRIS TO USE CLASS F1&F2
Address: SUTTON AMBULANCE STATION, DORSET ROAD, SUTTON, LONDON, SM2 6JH
Drawing title: PROPOSED REFUSE DETAIL

Scale: 1 : 50 @ A1
Date: 29/05/25
Drawn by: MA / OI
Drawing num: 786/BASMA/PP -360
Rev:

Office 3 (Ground floor) 679-691 High Road, Leyton, London E10 6RA
Tel. 020 8558 4272